






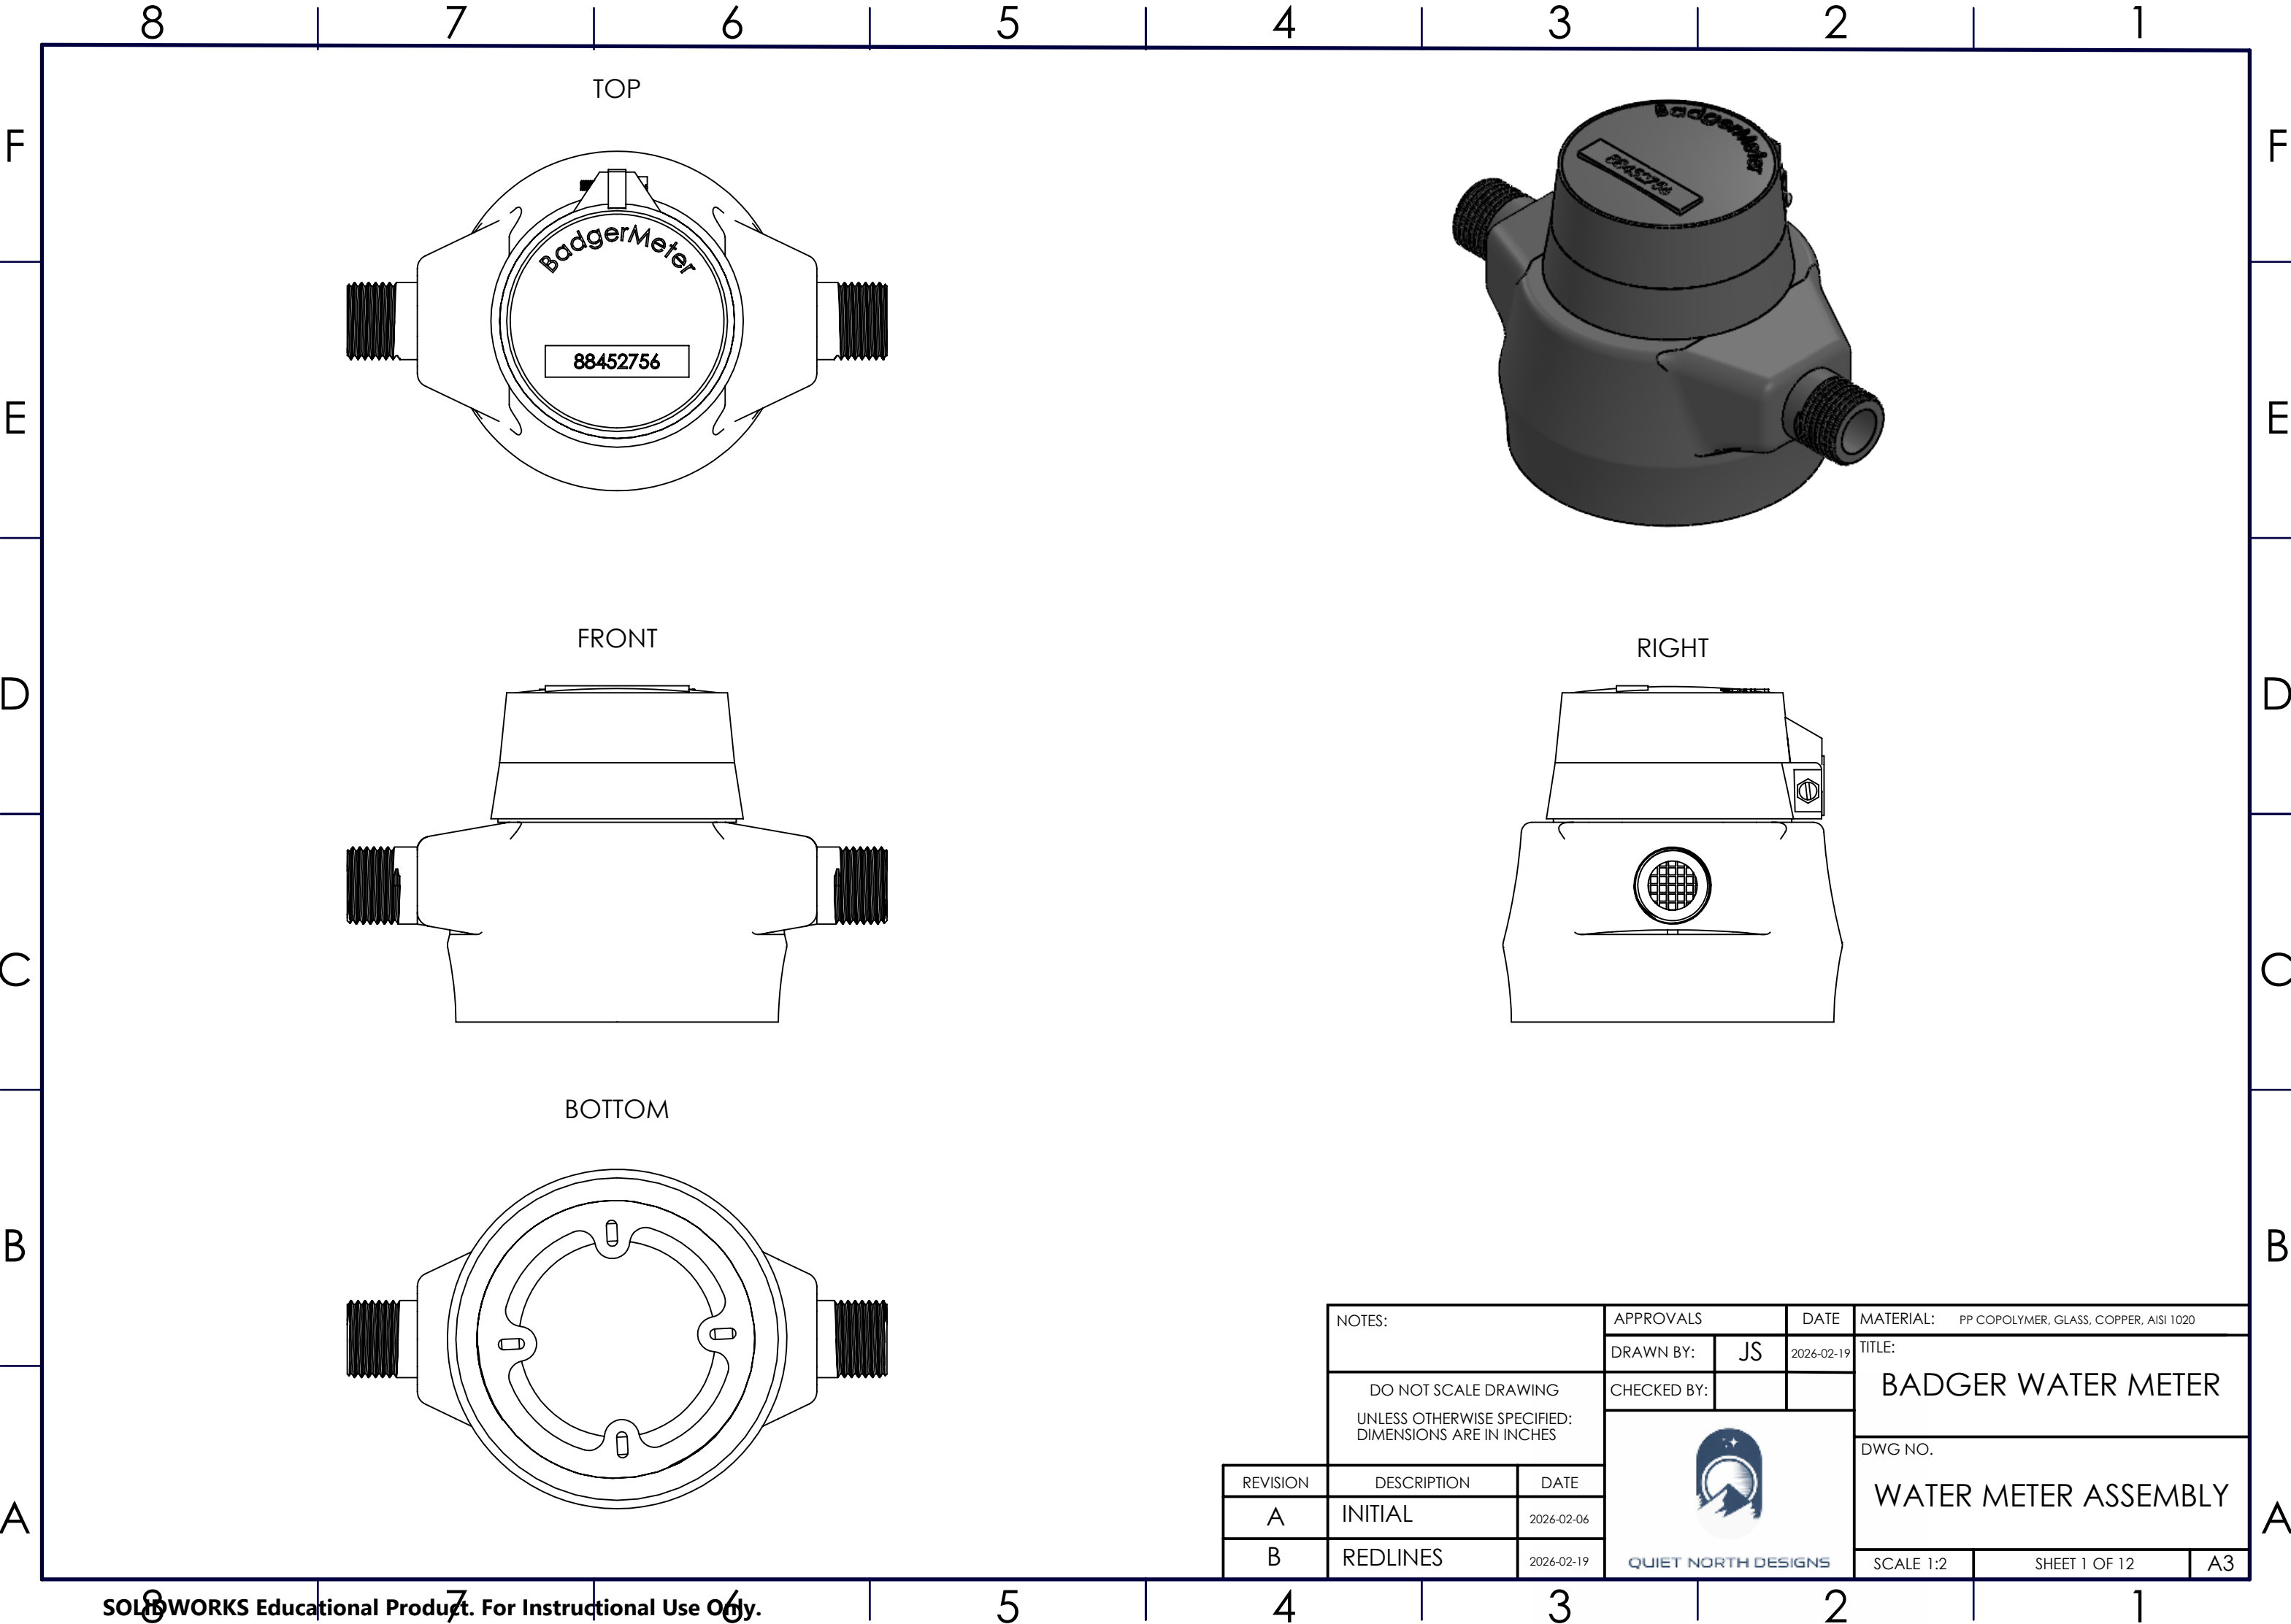


NOTES: DO NOT SCALE DRAWING UNLESS OTHERWISE SPECIFIED: DIMENSIONS ARE IN INCHES	APPROVALS		DATE	MATERIAL: PP COPOLYMER, GLASS, COPPER, AISI 1020
	DRAWN BY:	JS	2026-02-19	TITLE:
 QUIET NORTH DESIGNS	CHECKED BY:			BADGER WATER METER
				DWG NO.
REVISION	DESCRIPTION	DATE	WATER METER ASSEMBLY	
A	INITIAL	2026-02-06		
B	REDLINES	2026-02-19		
			SCALE 1:2	SHEET 1 OF 12
			A3	



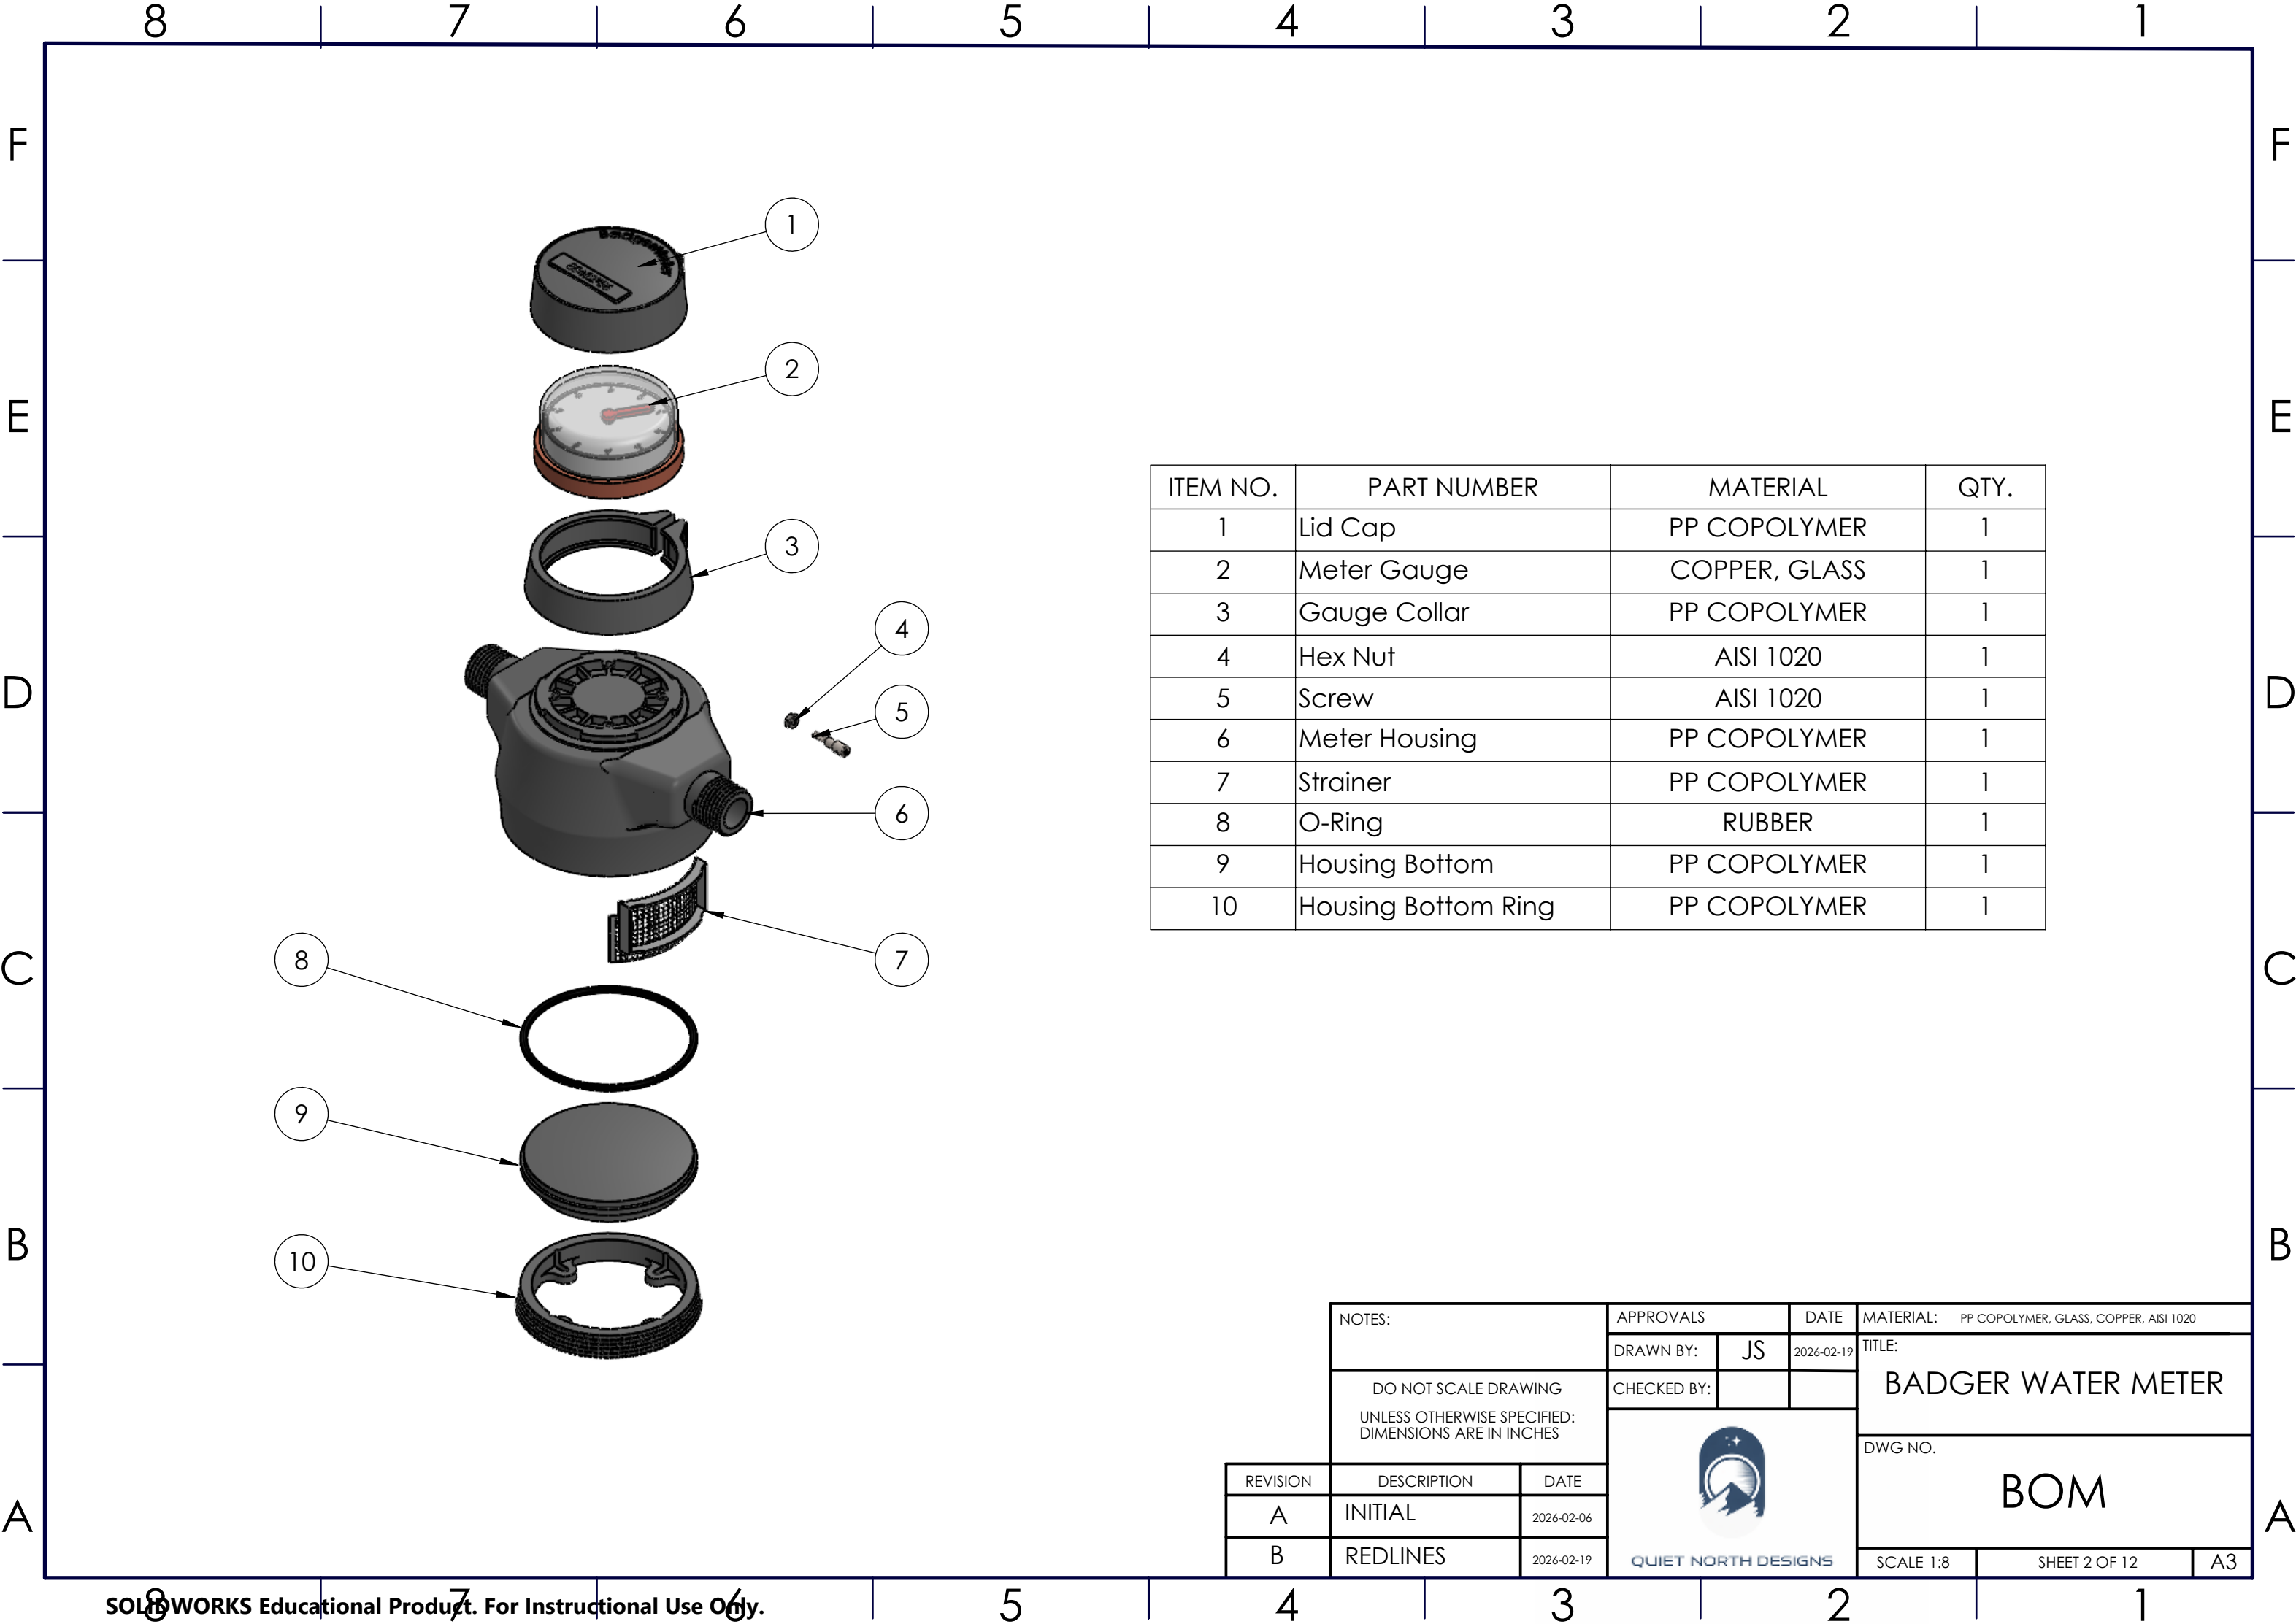


ITEM NO.	PART NUMBER	MATERIAL	QTY.
1	Lid Cap	PP COPOLYMER	1
2	Meter Gauge	COPPER, GLASS	1
3	Gauge Collar	PP COPOLYMER	1
4	Hex Nut	AISI 1020	1
5	Screw	AISI 1020	1
6	Meter Housing	PP COPOLYMER	1
7	Strainer	PP COPOLYMER	1
8	O-Ring	RUBBER	1
9	Housing Bottom	PP COPOLYMER	1
10	Housing Bottom Ring	PP COPOLYMER	1

NOTES: DO NOT SCALE DRAWING UNLESS OTHERWISE SPECIFIED: DIMENSIONS ARE IN INCHES			APPROVALS		DATE	MATERIAL: PP COPOLYMER, GLASS, COPPER, AISI 1020				
			DRAWN BY:	JS	2026-02-19	TITLE:				
			CHECKED BY:			BADGER WATER METER				
REVISION A INITIAL 2026-02-06 B REDLINES 2026-02-19			 QUIET NORTH DESIGNS			DWG NO.				
						BOM				
						SCALE 1:8		SHEET 2 OF 12		A3


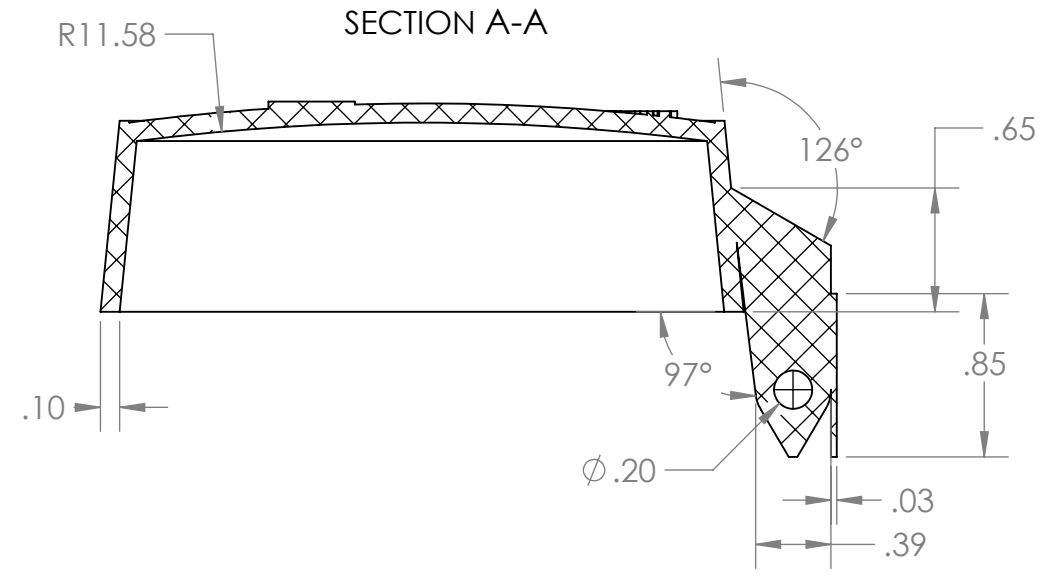
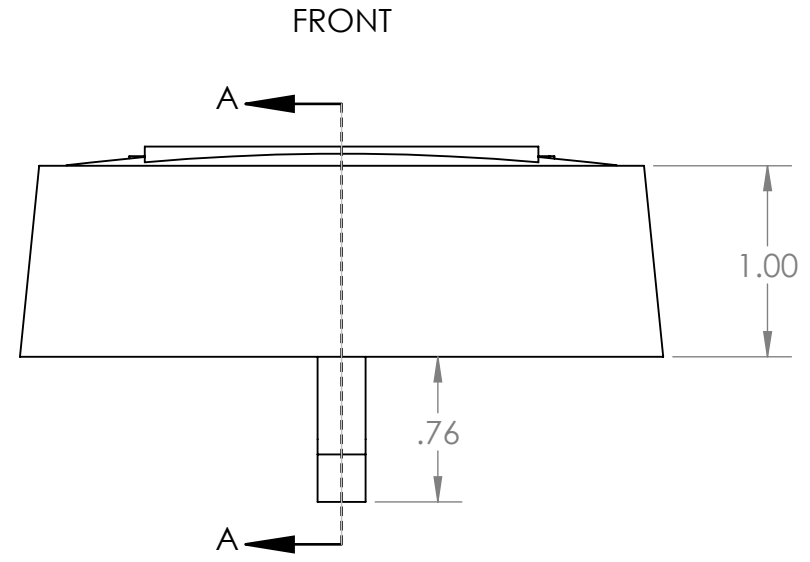
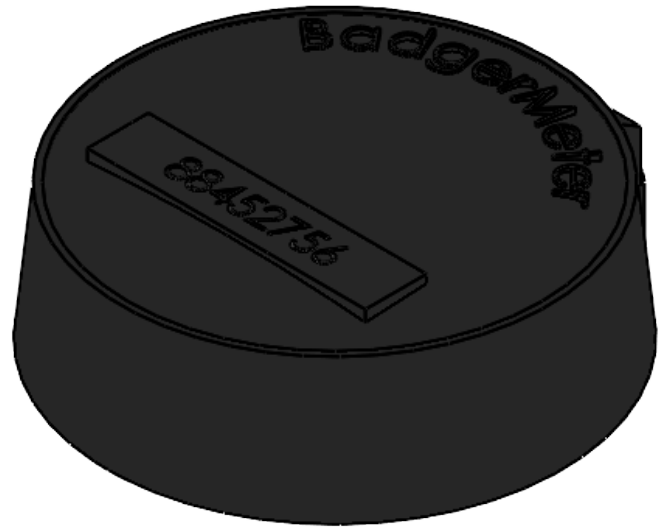
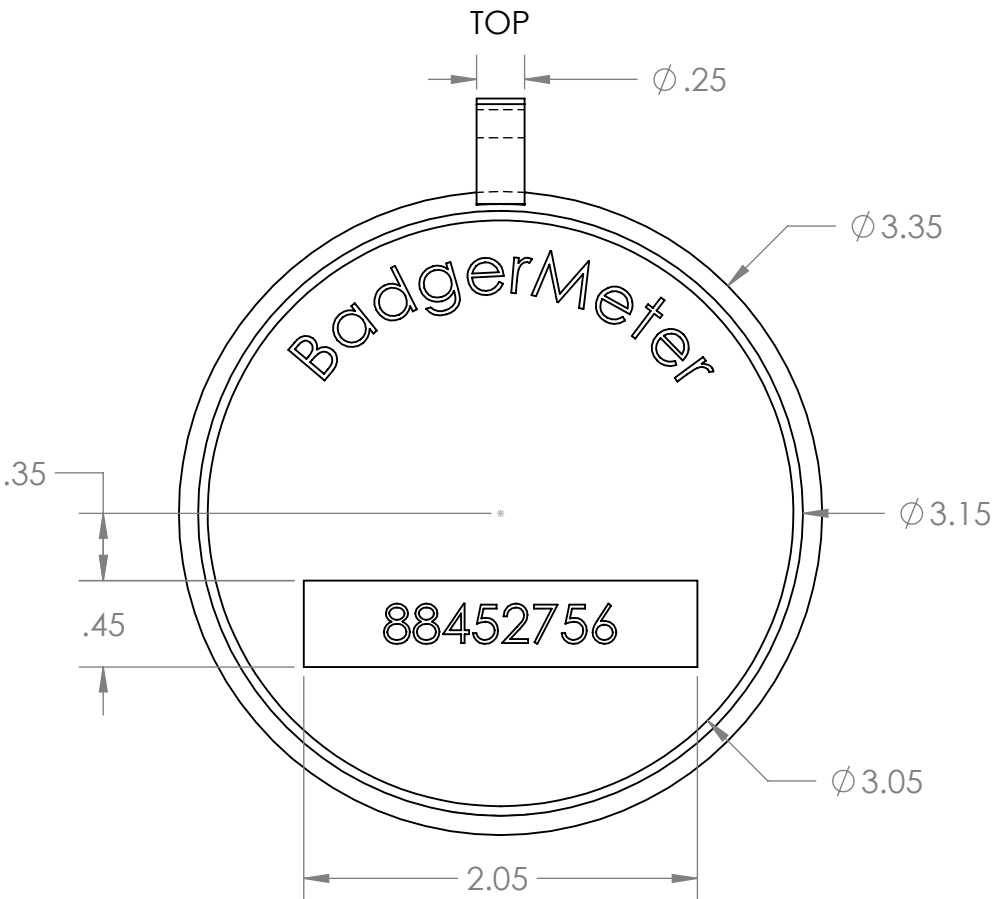


NOTES: DO NOT SCALE DRAWING UNLESS OTHERWISE SPECIFIED: DIMENSIONS ARE IN INCHES			APPROVALS		DATE		MATERIAL: PP COPOLYMER					
			DRAWN BY: JS		2026-02-19		TITLE: BADGER WATER METER					
			CHECKED BY:									
			 QUIET NORTH DESIGNS		DWG NO. LID CAP							
REVISION	DESCRIPTION	DATE			SCALE 1:1				SHEET 3 OF 12		A3	
A	INITIAL	2026-02-06										
B	REDLINES	2026-02-19										

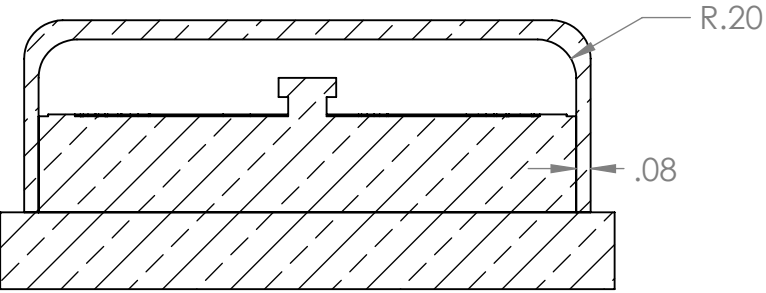
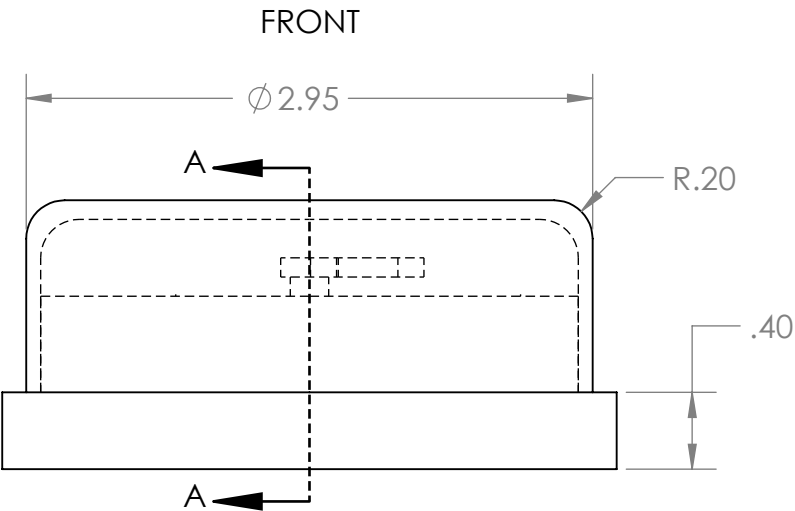
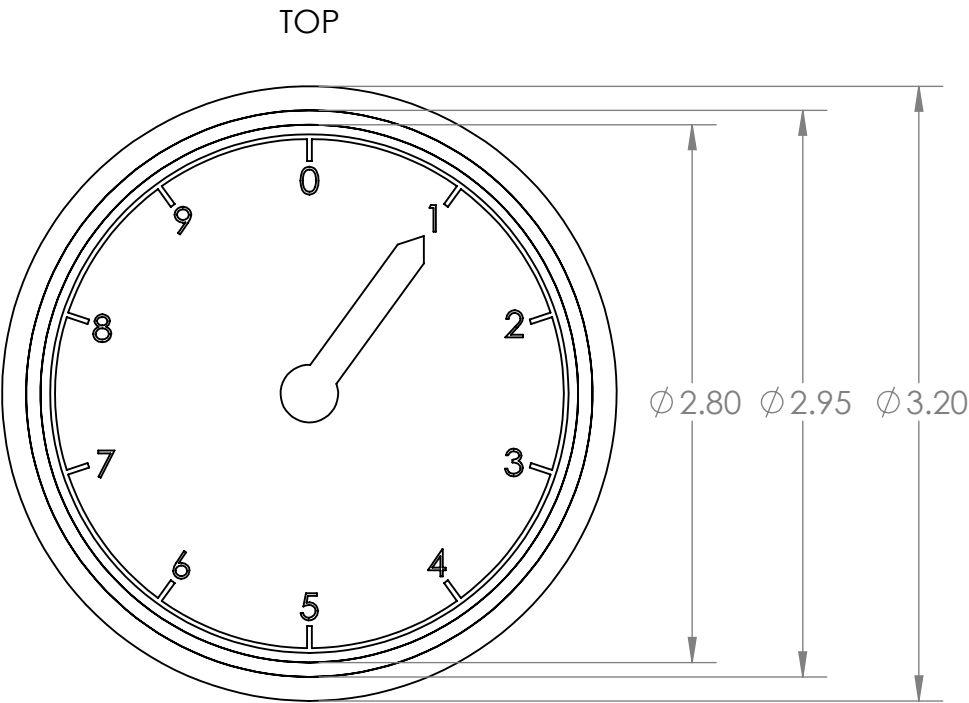


SECTION A-A


NOTES: DO NOT SCALE DRAWING UNLESS OTHERWISE SPECIFIED: DIMENSIONS ARE IN INCHES			APPROVALS		DATE	MATERIAL: COPPER, GLASS		
			DRAWN BY:	JS	2026-02-19	TITLE:		
			CHECKED BY:			BADGER WATER METER		
REVISIONDESCRIPTIONDATE AINITIAL2026-02-06 BREDLINES2026-02-19								
						METER GAUGE		
						SHEET 4 OF 12		

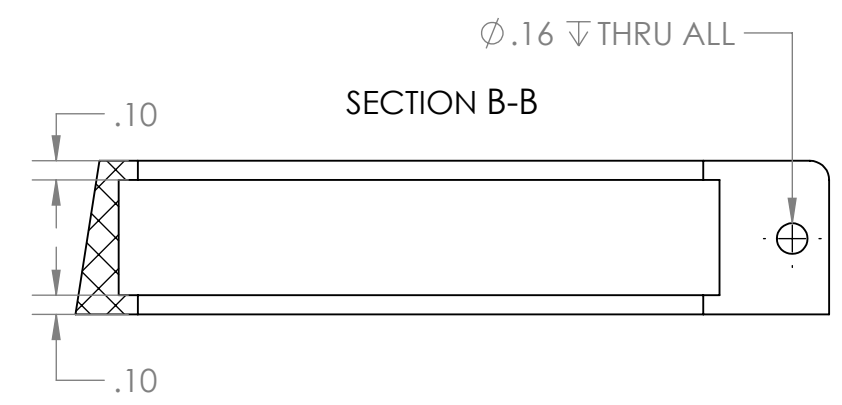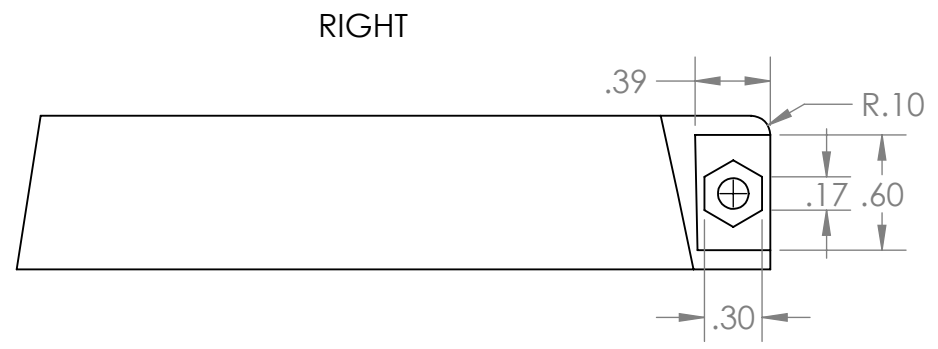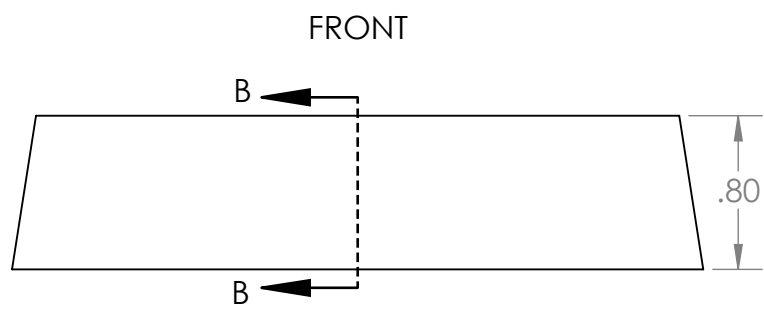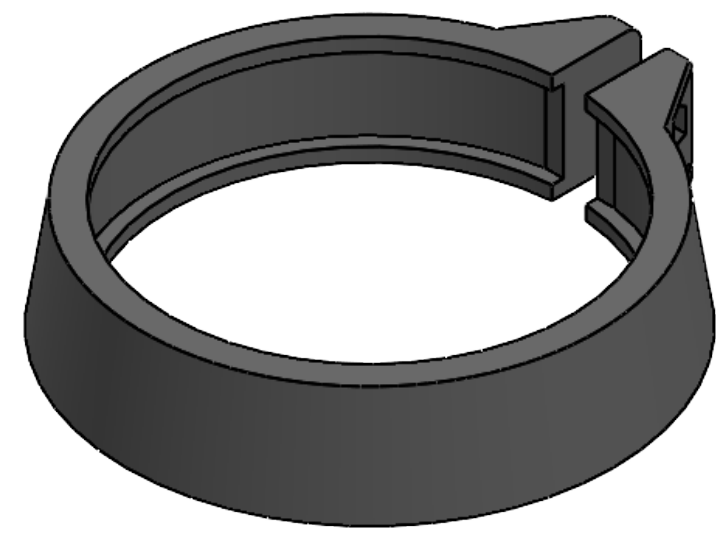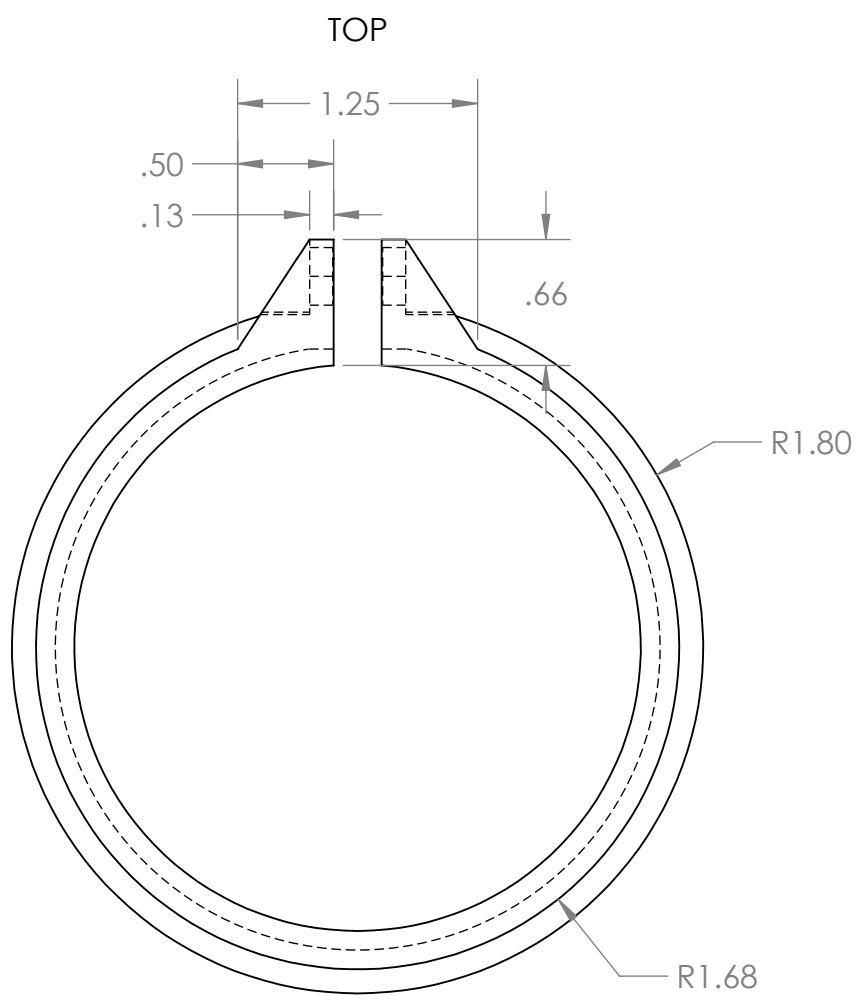




NOTES:		APPROVALS		DATE	MATERIAL: PP COPOLYMER			
		DRAWN BY:	JS	2026-02-19	TITLE:			
DO NOT SCALE DRAWING UNLESS OTHERWISE SPECIFIED: DIMENSIONS ARE IN INCHES		CHECKED BY:			BADGER WATER METER			
		 QUIET NORTH DESIGNS						
DESCRIPTION					DATE	DWG NO.		
INITIAL					2026-02-06			
REDLINES					2026-02-19	SCALE 1:1		

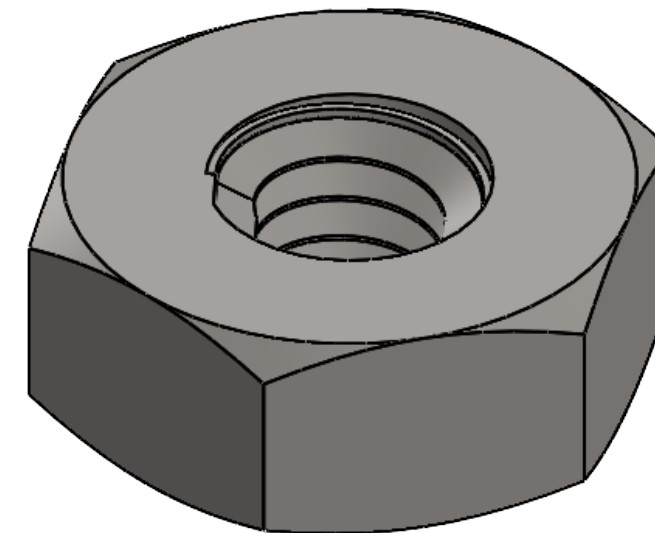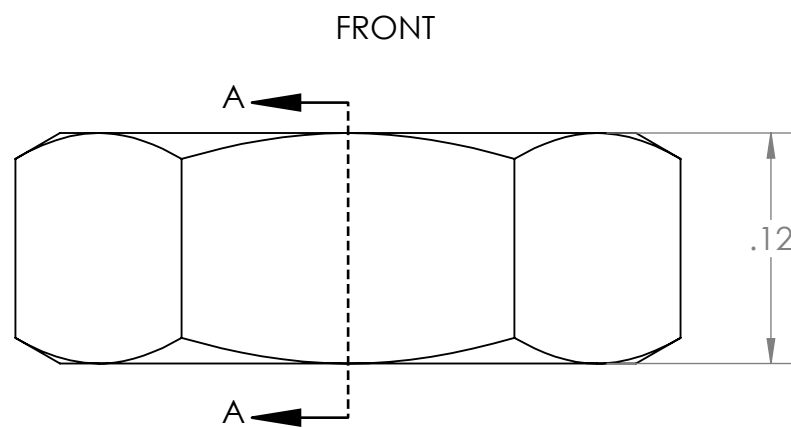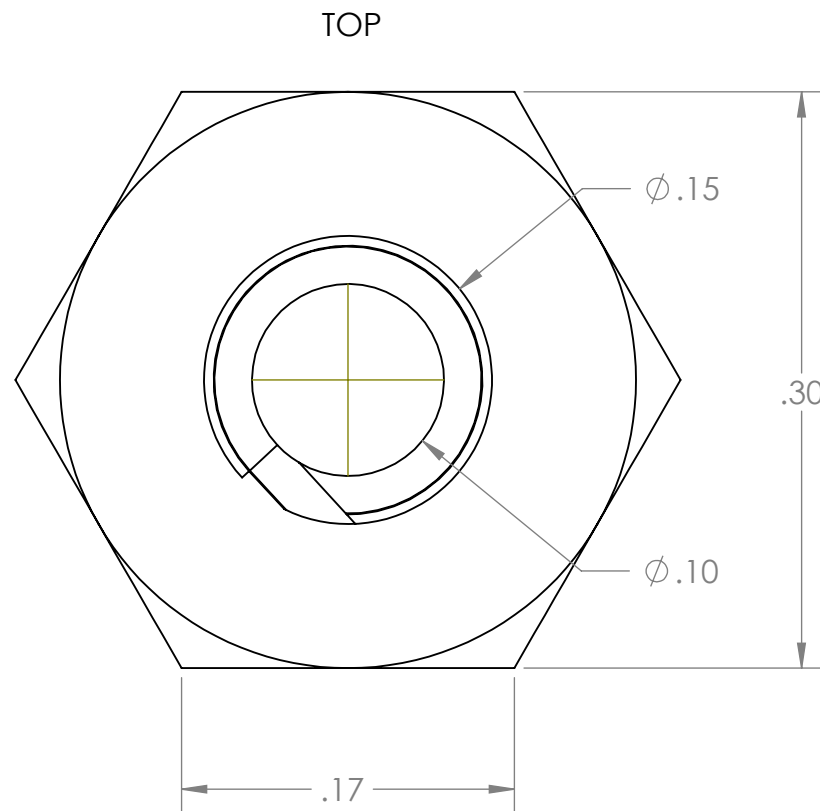


SECTION A-A
SCALE 10 : 1

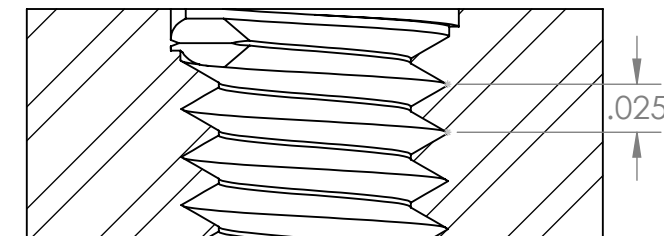


NOTES:			APPROVALS		DATE	MATERIAL: AISI 1020					
			DRAWN BY:	JS	2026-02-19	TITLE: BADGER WATER METER					
DO NOT SCALE DRAWING UNLESS OTHERWISE SPECIFIED: DIMENSIONS ARE IN INCHES			CHECKED BY:						DWG NO. HEX NUT		
			 QUIET NORTH DESIGNS			SCALE 10:1					
REVISION	DESCRIPTION	DATE									
A	INITIAL	2026-02-06									
B	REDLINES	2026-02-19									

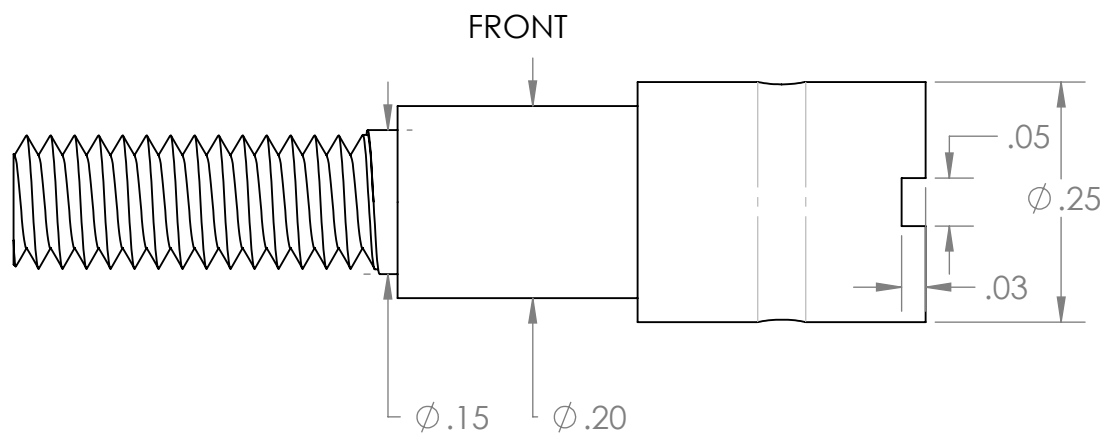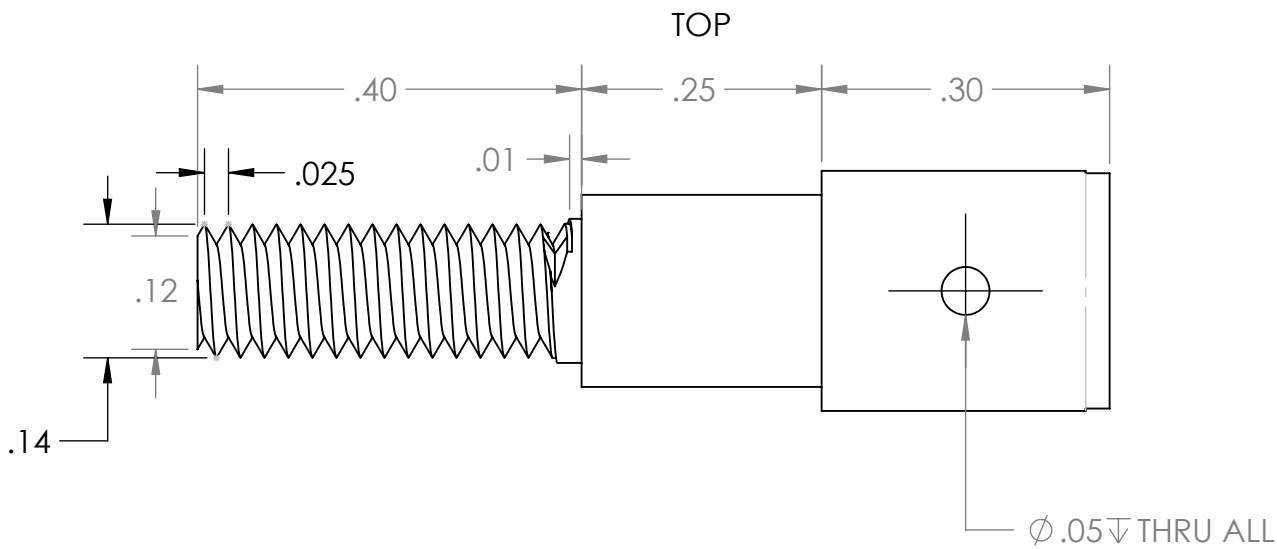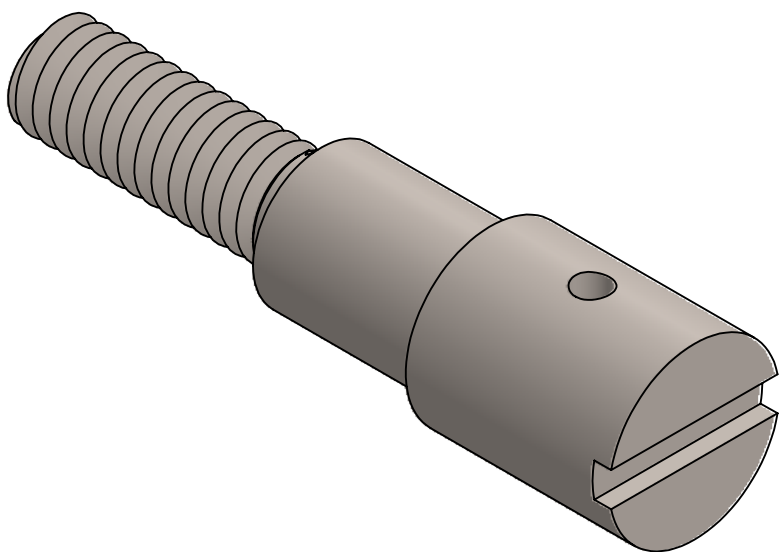





RIGHT

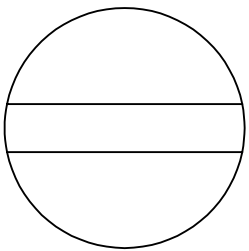

NOTES: DO NOT SCALE DRAWING UNLESS OTHERWISE SPECIFIED: DIMENSIONS ARE IN INCHES	APPROVALS		DATE	MATERIAL: AISI 1020	
			DRAWN BY: JS	2026-02-19	TITLE: BADGER WATER METER
			CHECKED BY:		DWG NO. SCREW
REVISION	DESCRIPTION	DATE	 QUIET NORTH DESIGNS		
A	INITIAL	2026-02-06			
B	REDLINES	2026-02-19			
			SCALE 5:1	SHEET 7 OF 12	A3

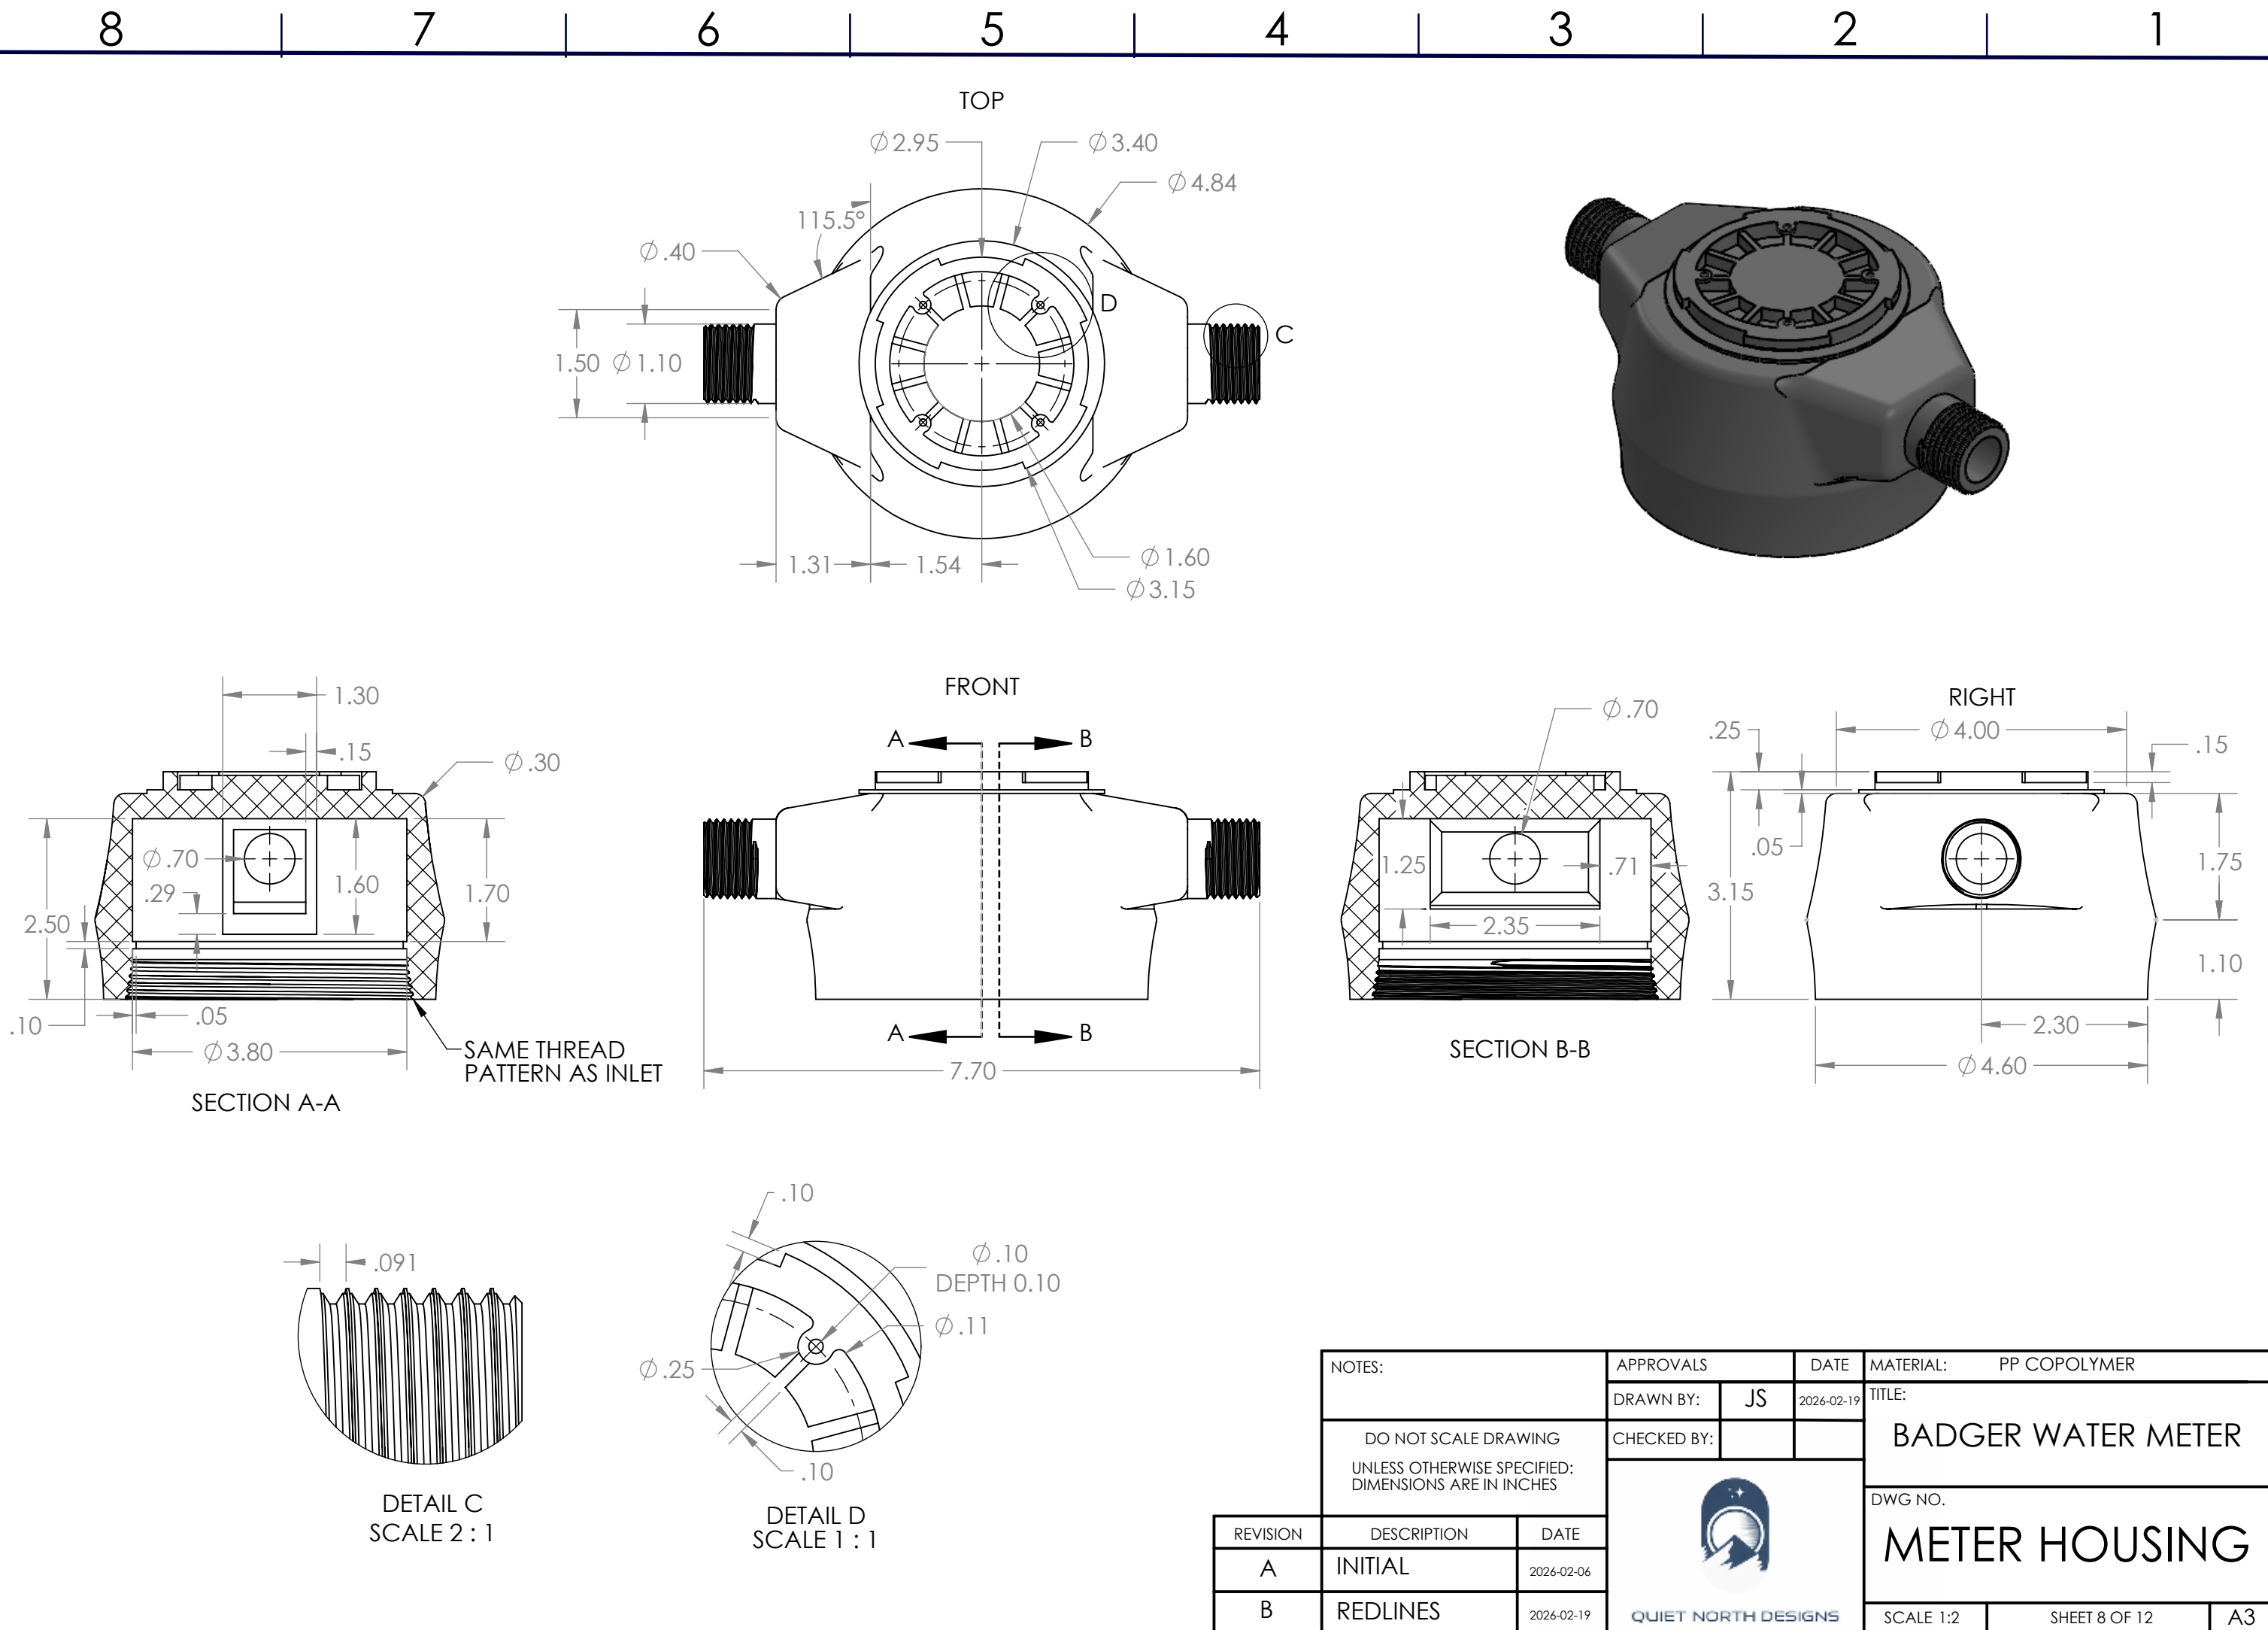


	NOTES:		APPROVALS		DATE	MATERIAL: PP COPOLYMER	
			DRAWN BY:	JS	2026-02-19	TITLE:	
	DO NOT SCALE DRAWING UNLESS OTHERWISE SPECIFIED: DIMENSIONS ARE IN INCHES		CHECKED BY:			BADGER WATER METER	
			 QUIET NORTH DESIGNS			DWG NO.	
						METER HOUSING	
REVISION	DESCRIPTION	DATE					
A	INITIAL	2026-02-06					
B	REDLINES	2026-02-19			SCALE 1:2	SHEET 8 OF 12	A3

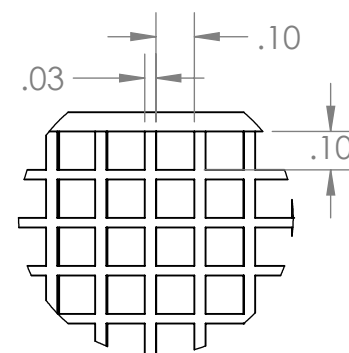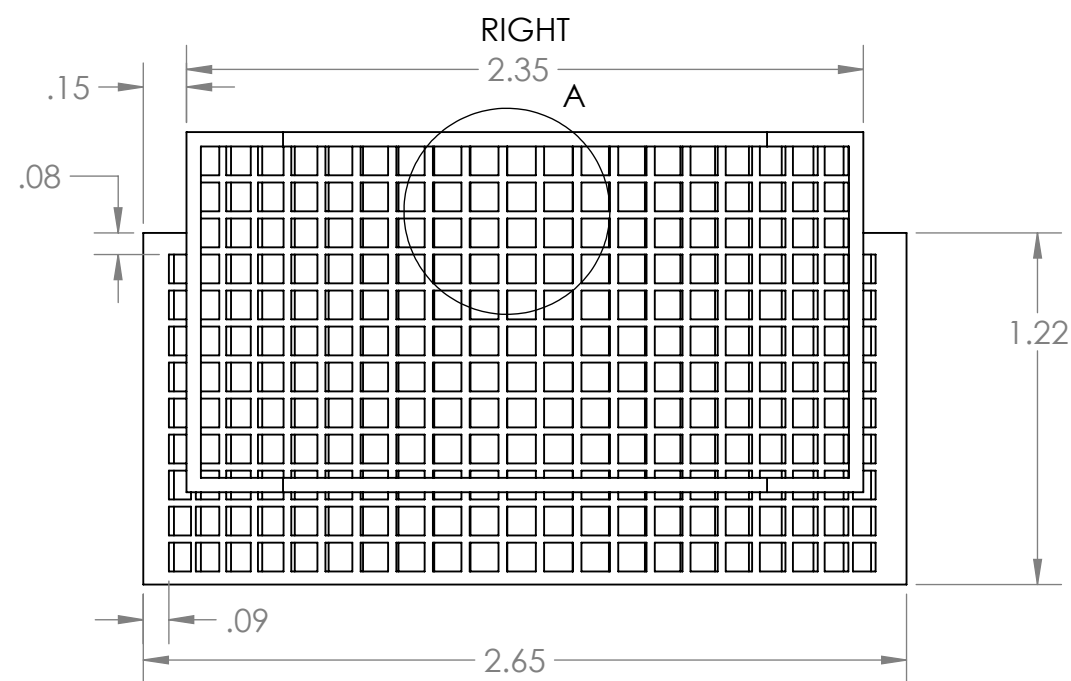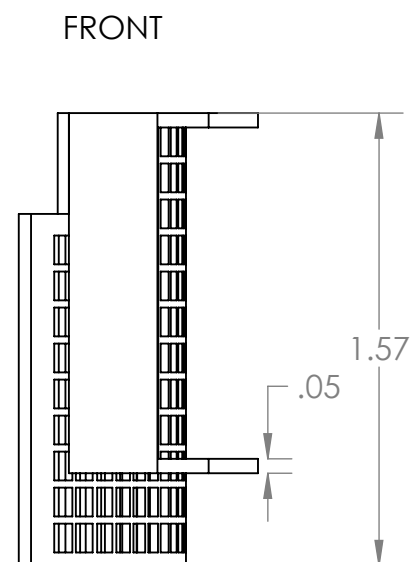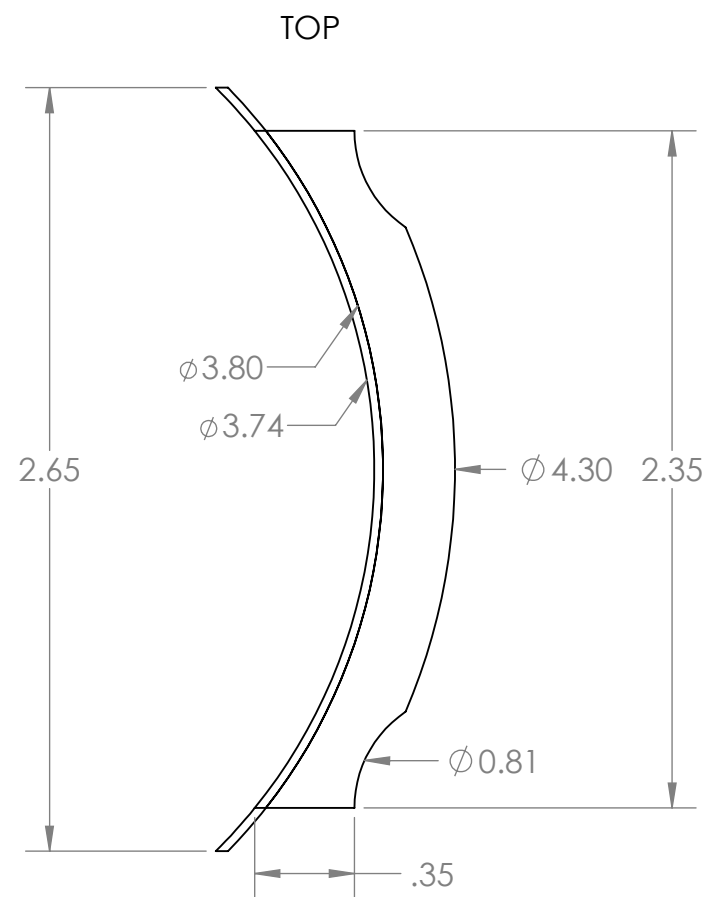


DETAIL A
SCALE 2 : 1

NOTES: DO NOT SCALE DRAWING UNLESS OTHERWISE SPECIFIED: DIMENSIONS ARE IN INCHES	APPROVALS		DATE	MATERIAL: PP COPOLYMER
	DRAWN BY:	JS	2026-02-19	TITLE:
	CHECKED BY:			BADGER WATER METER
	 QUIET NORTH DESIGNS			DWG NO.
				STRAINER
REVISION	DESCRIPTION	DATE	SCALE 1.5:1	
A	INITIAL	2026-02-06	SHEET 9 OF 12	
B	REDLINES	2026-02-19	A3	



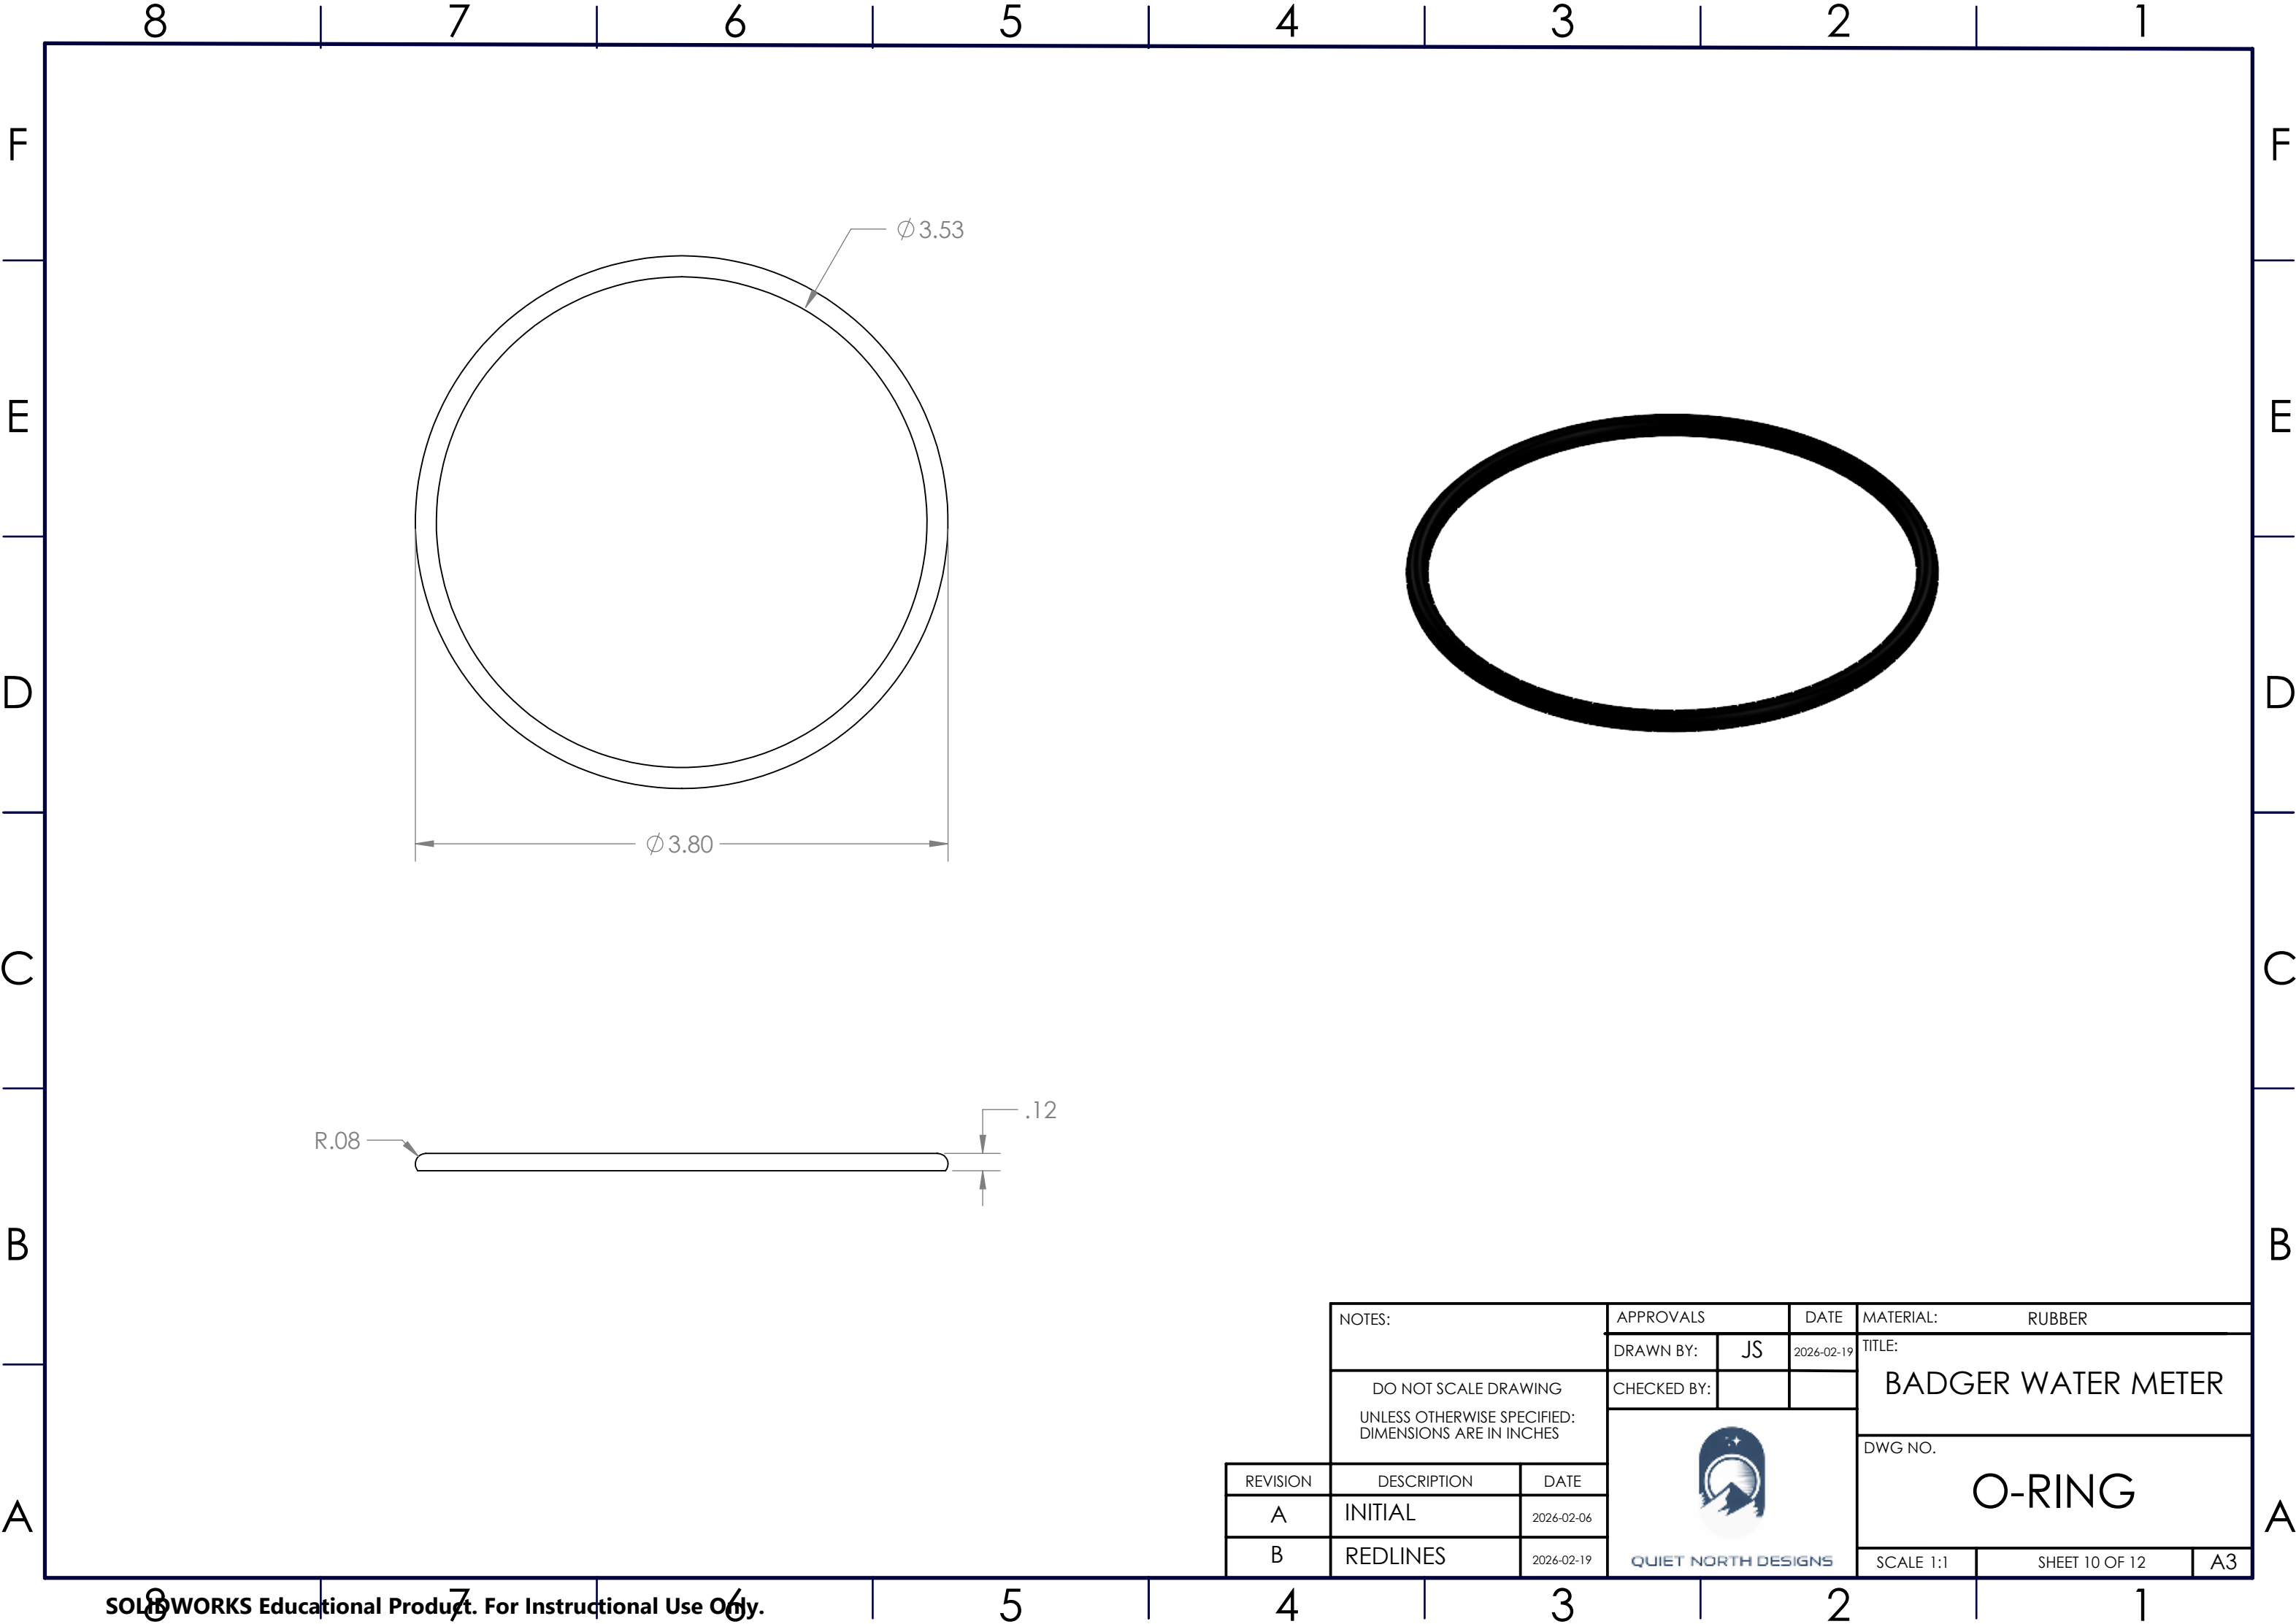


NOTES: DO NOT SCALE DRAWING UNLESS OTHERWISE SPECIFIED: DIMENSIONS ARE IN INCHES			APPROVALS		DATE	MATERIAL: RUBBER		
			DRAWN BY:	JS	2026-02-19	TITLE:		
			CHECKED BY:			BADGER WATER METER		
			 QUIET NORTH DESIGNS			DWG NO.		
						O-RING		
REVISION	DESCRIPTION	DATE						
A	INITIAL	2026-02-06						
B	REDLINES	2026-02-19						
			SCALE 1:1		SHEET 10 OF 12		A3	

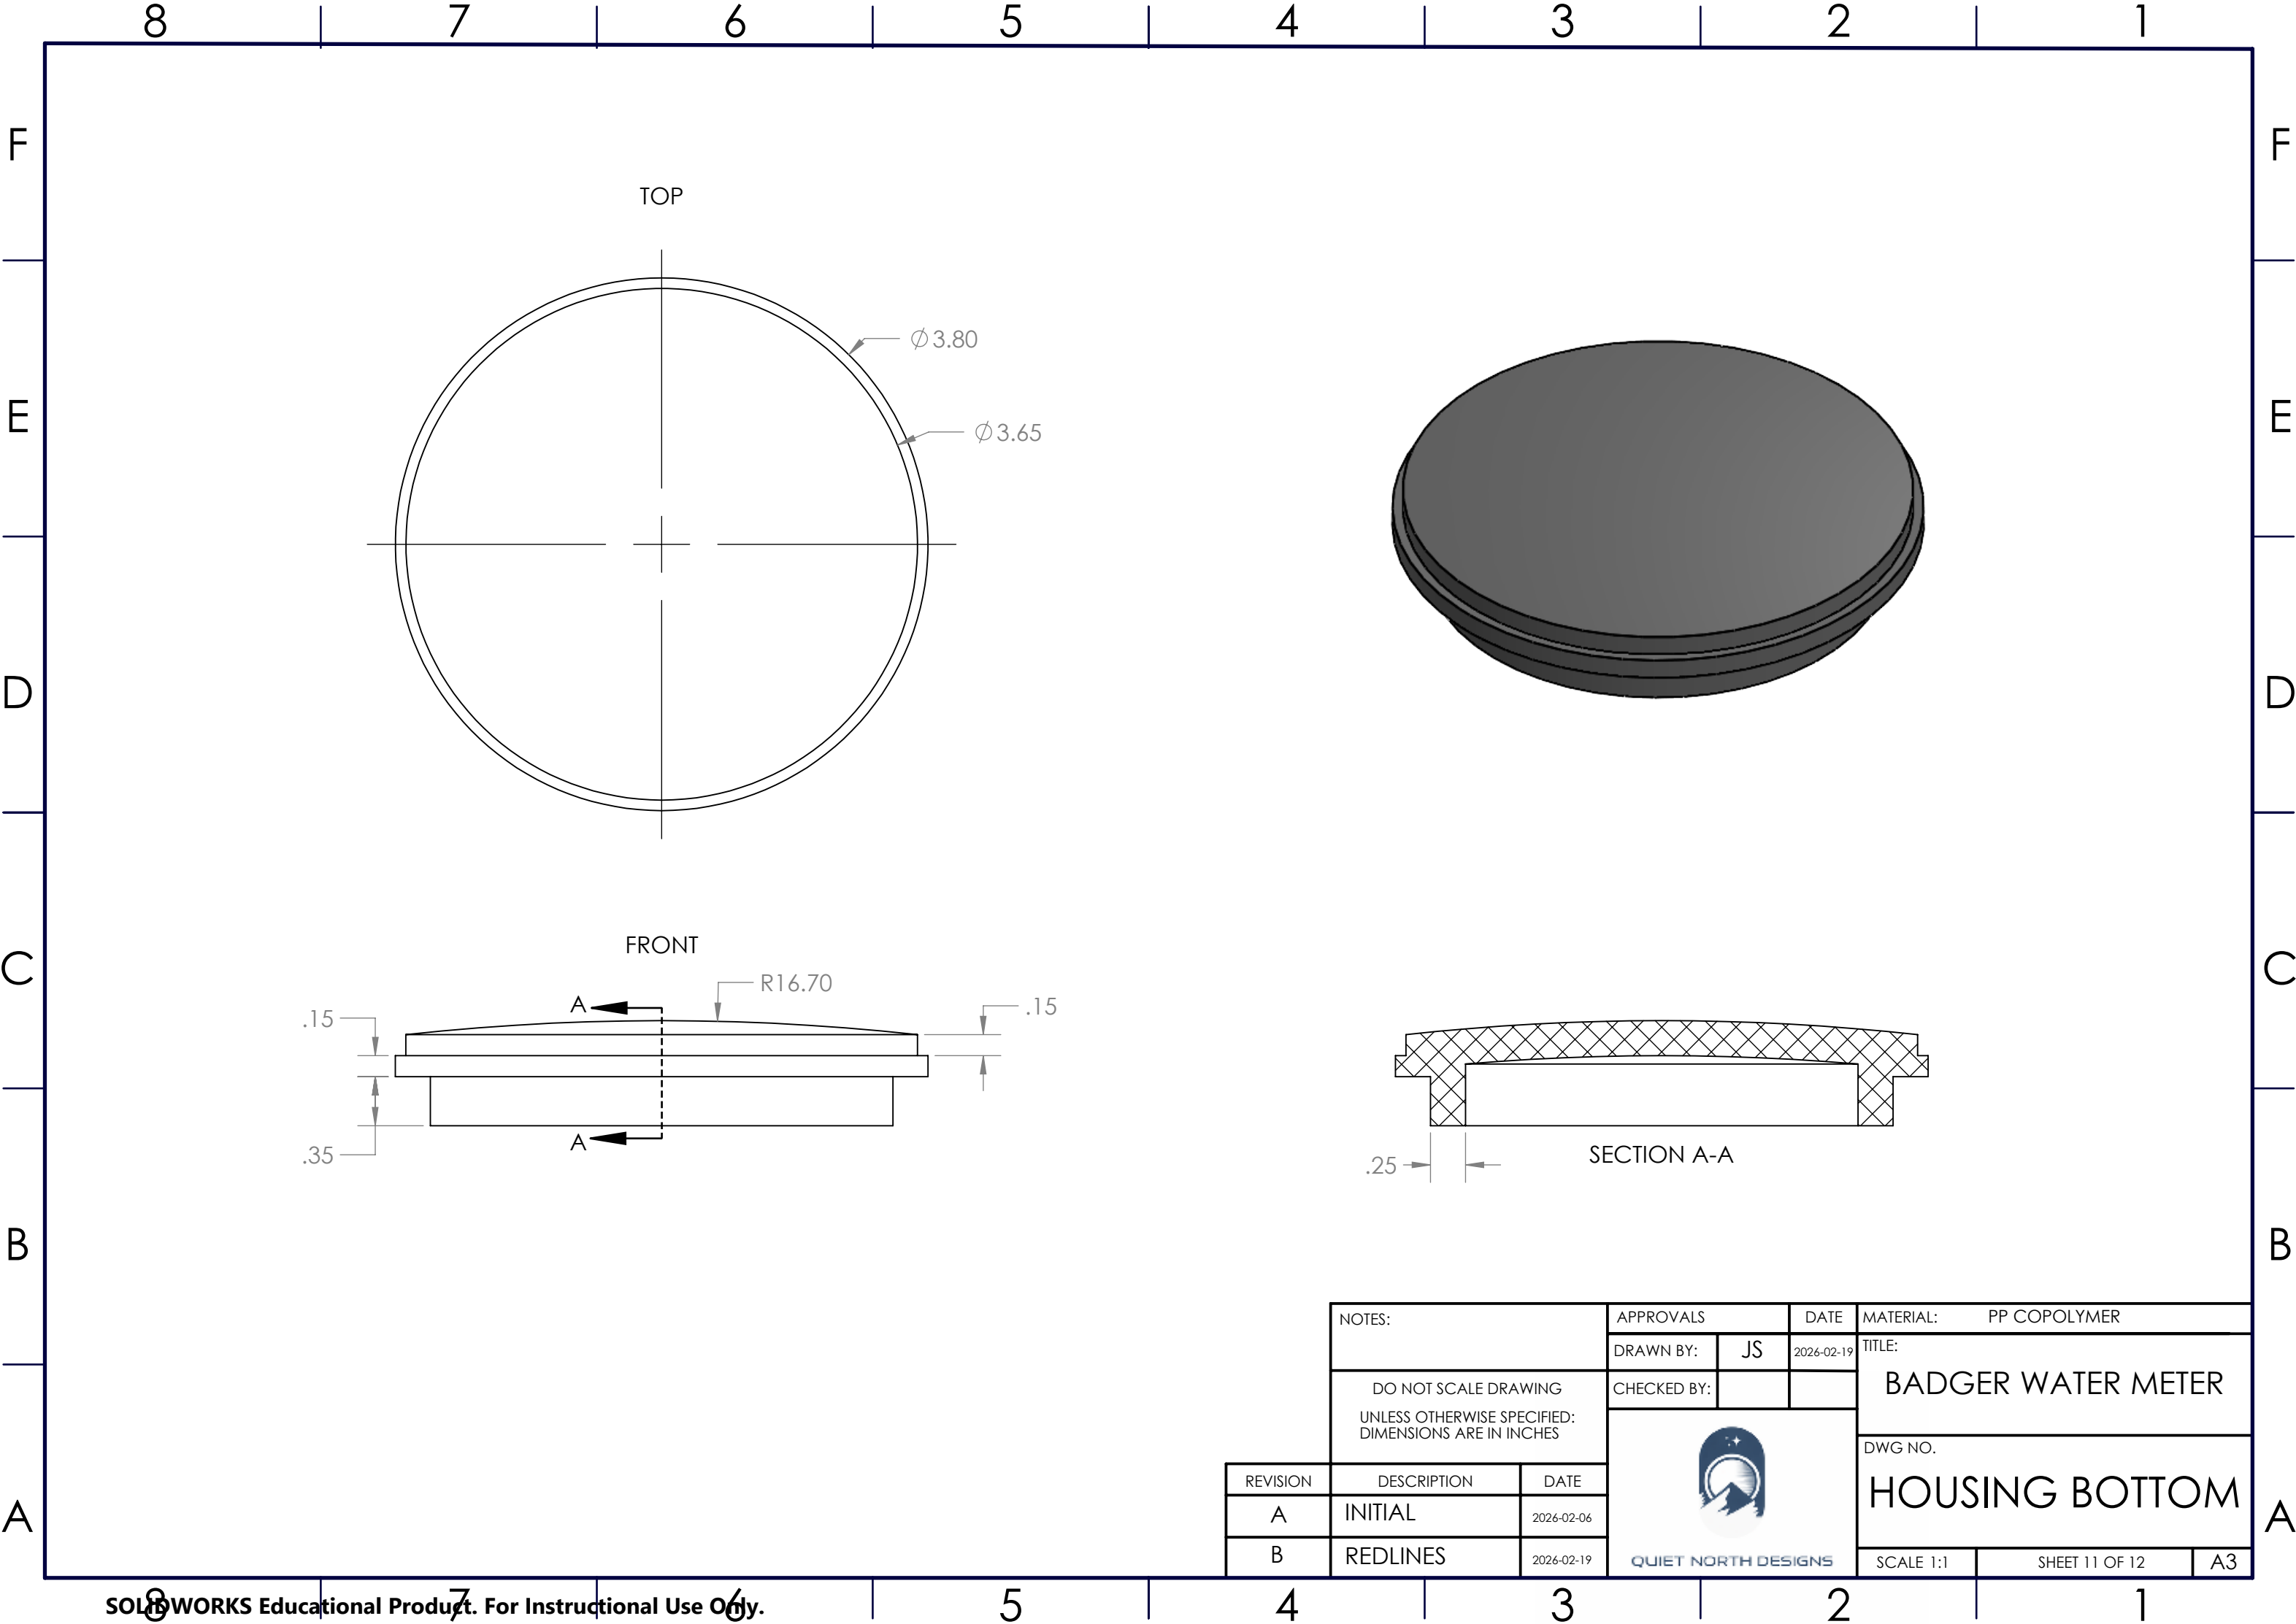


NOTES: DO NOT SCALE DRAWING UNLESS OTHERWISE SPECIFIED: DIMENSIONS ARE IN INCHES	APPROVALS		DATE	MATERIAL: PP COPOLYMER
	DRAWN BY:	JS	2026-02-19	TITLE:
			CHECKED BY:	
			BADGER WATER METER	
			DWG NO.	
			HOUSING BOTTOM	
			SCALE 1:1	SHEET 11 OF 12
			A3	



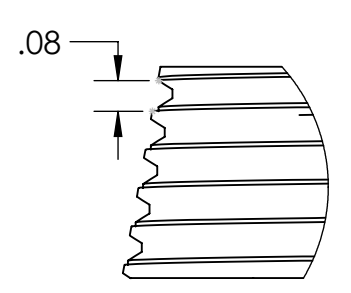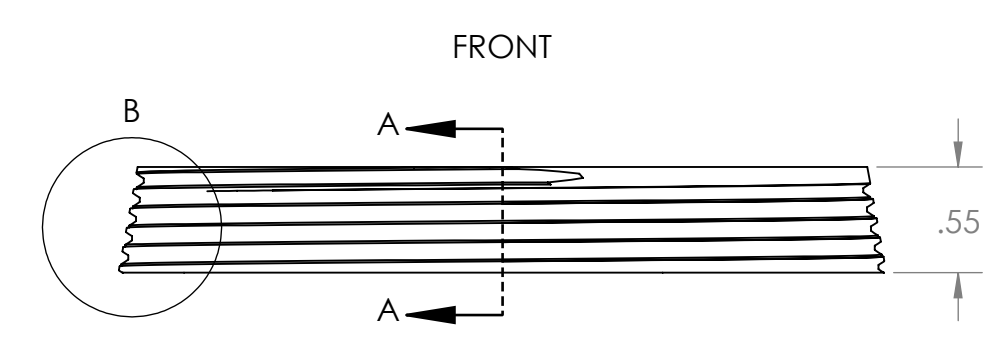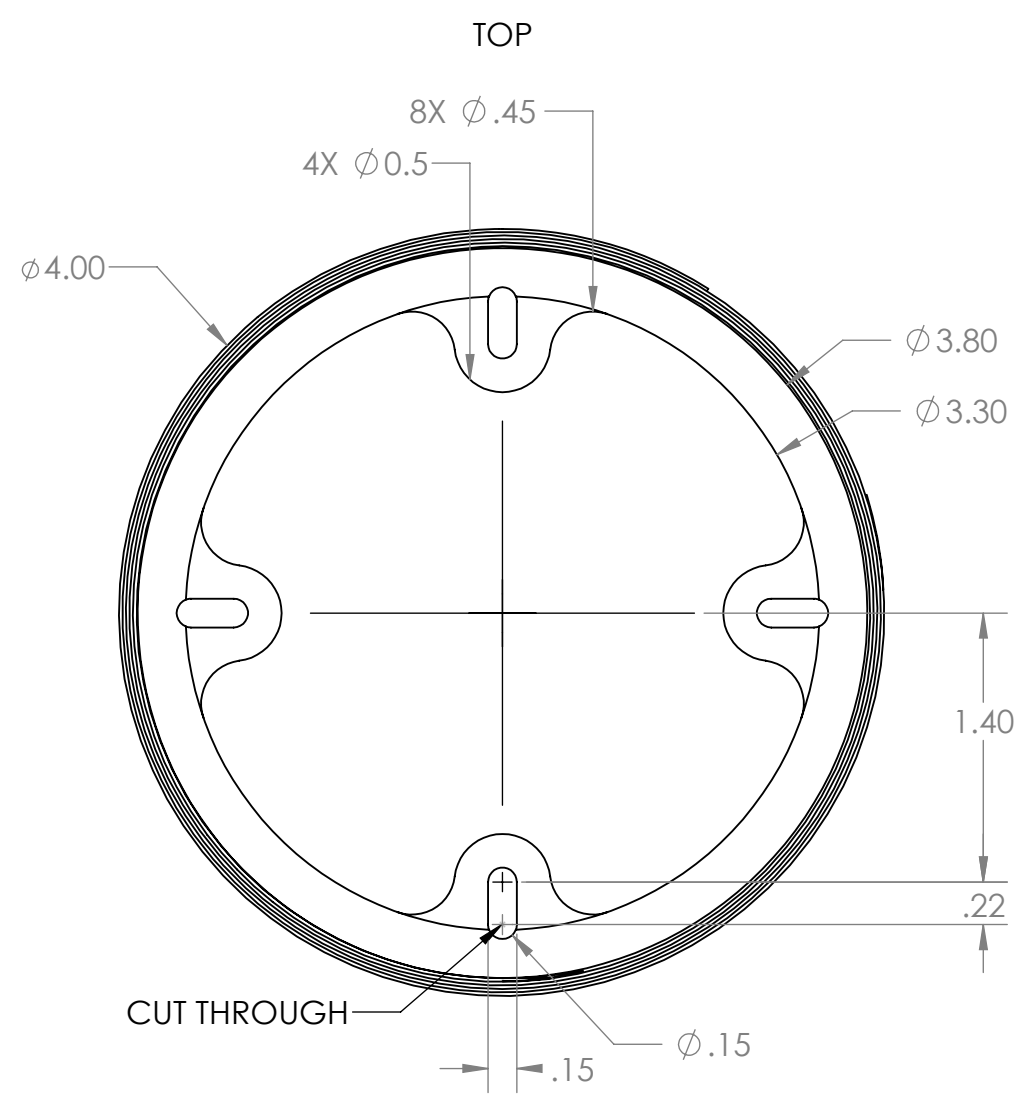

DETAIL B
SCALE 2 : 1

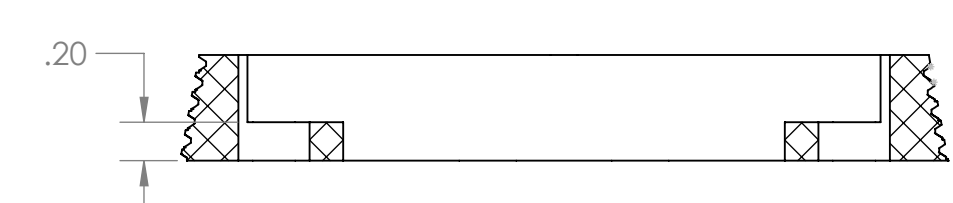

SECTION A-A

NOTES:		APPROVALS		DATE	MATERIAL: PP COPOLYMER		
		DRAWN BY:	JS	2026-02-19	TITLE: BADGER WATER METER		
DO NOT SCALE DRAWING UNLESS OTHERWISE SPECIFIED: DIMENSIONS ARE IN INCHES		CHECKED BY:					DWG NO. HOUSING BOTTOM RING
		 QUIET NORTH DESIGNS					
DESCRIPTION					DATE		
INITIAL					2026-02-06		
REDLINES		2026-02-19		SCALE 1:1			
				SHEET 12 OF 12		A3	